
Authentisign ID: 0892CC4F-2BC8-F111-BF5B-000D3A4FF82A

LAND TITLE SURVEY

16241 COUNTY ROAD 1322, FLINT, TEXAS 76762

BEING ALL THAT CERTAIN LOT TRACT OR PARCEL OF LAND LOCATED IN THE P.E. BEAN LEAGUE SURVEY, A-2, SMITH COUNTY, TEXAS, BEING DESCRIBED AS PART OF A CALLED 0.357 ACRE TRACT OF LAND DESCRIBED IN DEED TO THOMAS H. & LINDA J. ALEXANDER RECORDED IN DOCUMENT * 2013-57719, OF THE DEED RECORDS SMITH COUNTY, TEXAS (DRSCT).

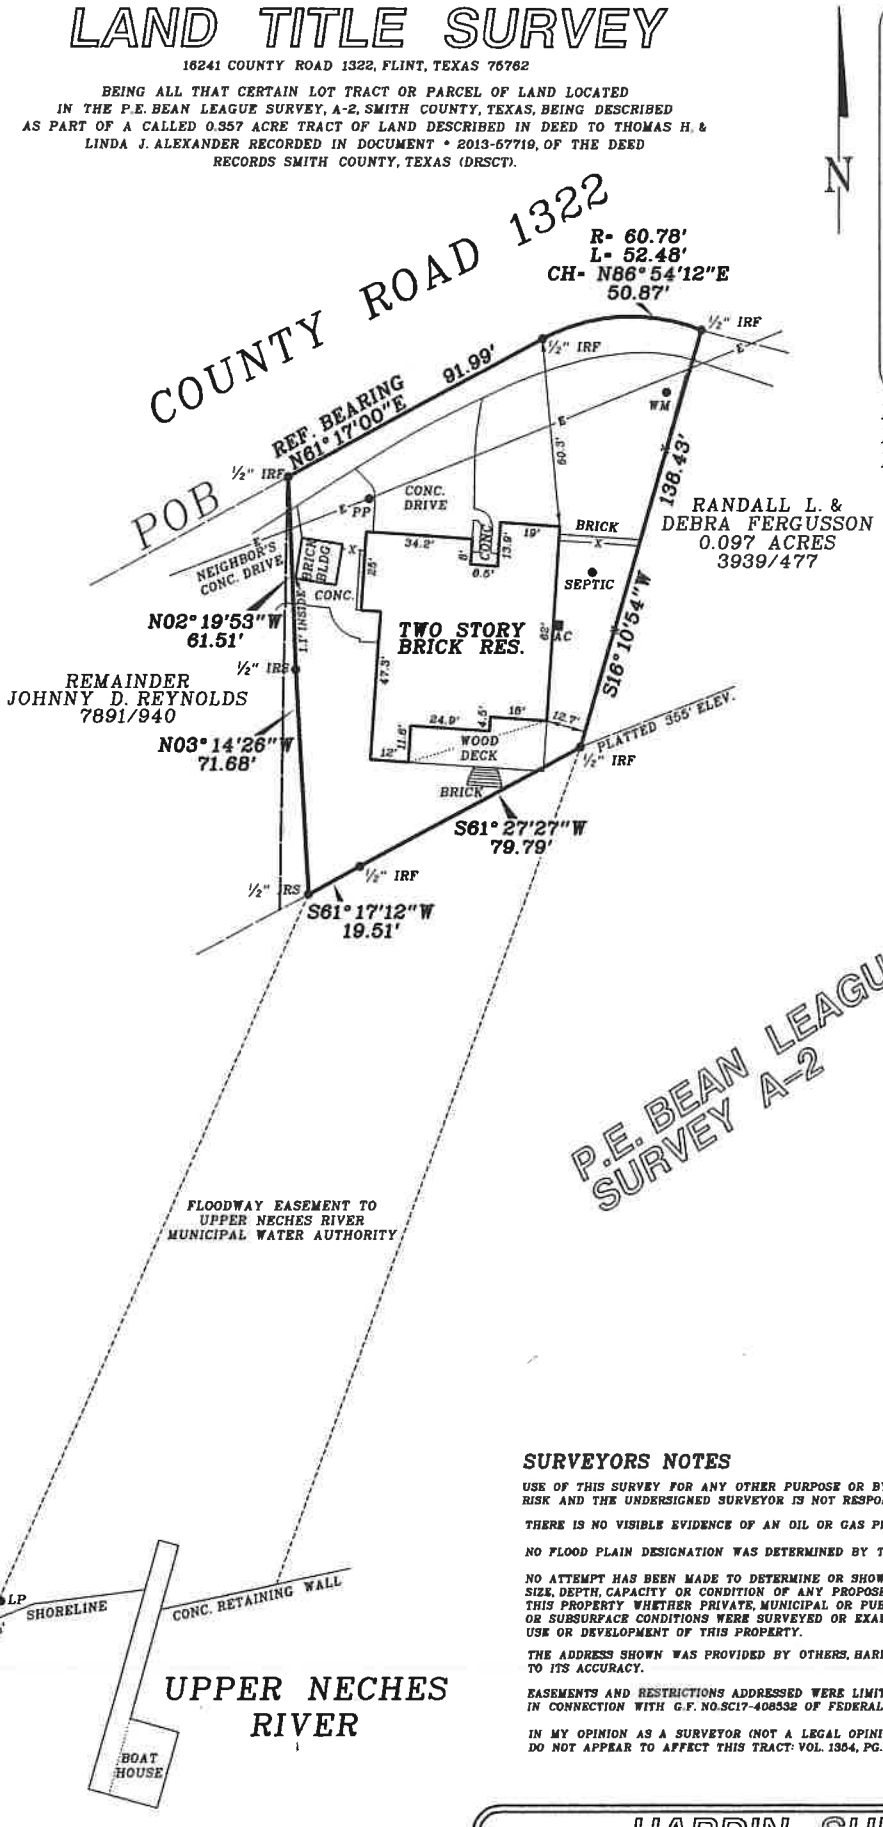

LEGEND

TELEPHONE LINE
CABLE LINE
FENCE
POWER LINE

CONC. - CONCRETE
PP - POWER POLE
WM - WATER METER
IRF - IRON ROD FOUND
IRS - IRON ROD SET W/CAP * 4207
IPF - IRON PIPE FOUND
FC - FENCE CORNER FOUND
TB - TELEPHONE BOX
LP - LIGHT POLE
BCS - BURIED CABLE SIGN
GM - GAS METER
EB - ELECTRICAL BOX
PT - PROPANE TANK
SP - SERVICE POLE
FH - FIRE HYDRANT

BASIS OF BEARINGS:
DOCUMENT * 2013-57719
DRSCT

0.34 ACRES

SURVEYORS NOTES

USE OF THIS SURVEY FOR ANY OTHER PURPOSE OR BY OTHER PARTIES SHALL BE AT THEIR OWN RISK AND THE UNDERSIGNED SURVEYOR IS NOT RESPONSIBLE FOR ANY LOSS THEREFROM.

THERE IS NO VISIBLE EVIDENCE OF AN OIL OR GAS PIPELINE ON THIS TRACT.

NO FLOOD PLAIN DESIGNATION WAS DETERMINED BY THIS SURVEYOR.

NO ATTEMPT HAS BEEN MADE TO DETERMINE OR SHOW THE EXISTENCE, LOCATION, SIZE, DEPTH, CAPACITY OR CONDITION OF ANY PROPOSED OR EXISTING UTILITIES ON THIS PROPERTY WHETHER PRIVATE, MUNICIPAL OR PUBLICLY OWNED. NO ENVIRONMENTAL OR SUBSURFACE CONDITIONS WERE SURVEYED OR EXAMINED THAT MAY AFFECT THE USE OR DEVELOPMENT OF THIS PROPERTY.

THE ADDRESS SHOWN WAS PROVIDED BY OTHERS, HARDIN SURVEYING MAKES NO CLAIM TO ITS ACCURACY.

EASEMENTS AND RESTRICTIONS ADDRESSED WERE LIMITED TO THE FOLLOWING, IN CONNECTION WITH G.F. NO.SC17-408532 OF FEDERAL TITLE COMPANY.

IN MY OPINION AS A SURVEYOR (NOT A LEGAL OPINION) THE FOLLOWING DO NOT APPEAR TO AFFECT THIS TRACT: VOL. 1364, PG. 51

I GARY L. HARDIN R.P.L.S. * 4207, DO HEREBY CERTIFY THAT THE SURVEY SHOWN REPRESENTS THE RESULTS OF AN ON THE GROUND SURVEY MADE UNDER MY DIRECTION AND SUPERVISION DURING THE MONTH OF SEP. 2017, AND ALL CORNERS ARE SHOWN HEREON AND THERE ARE NO VISIBLE EASEMENTS, ENCROACHMENTS, CONFLICTS OR PROTRUSIONS OTHER THAN SHOWN.

GARY L. HARDIN R.P.L.S. * 4207
SIGNATURE VOID IF NOT SIGNED IN BLUE INK

© 2017 ALL RIGHTS RESERVED

SEE FIELD NOTES

FIRM REGISTRATION NO. 10114700

HARDIN SURVEYING
PO BOX 587
MABANK, TEXAS 75147
(903) 887-5674 LOCAL
(877) 329-6475 TOLL FREE
(903) 887-0421 FAX

DATE PERFORMED: SEPTEMBER 12, 2017
SCALE: 1"= 40 FEET
WORK ORDER * 1709018 DRAWN BY: JP/JH
FIELDED BY: JT CHECKED BY: TP
THIS SURVEY WAS PERFORMED FOR: HARDER

Authentisign ID: 0892CC4F-2BC8-F111-BF5B-000D3A4FF82A

FORM 51—6-1-68

W.A. 3088
E.R. 5
Proj. 166
Code 420/88

THE STATE OF TEXAS)
(12700
COUNTY OF Smith)

KNOW ALL MEN BY THESE PRESENTS: VOL 1354 PAGE 51

That Robert McKeethan

of Smith County, Texas, hereinafter called "Grantor," whether one or more, in consideration of the advantages which will accrue to Grantor from the construction of the electric power line and telephone line hereinafter described, hereby grants to TEXAS POWER & LIGHT COMPANY, of Dallas, Texas, and the an easement and right of way for an electric distribution line, consisting of variable numbers of wires, circuits, and all necessary or desirable appurtenances, and for a telephone line and appurtenances, upon over and across Grantor's land in the Pedro E. Bean Survey, Abstract No. 2, Smith County, Texas.

The center line of said distribution line and telephone line shall be located across said land as follows:

Beginning at a point in the north line of grantors property, same being the south right-of-way line of an oil county road. Said point being located 345 feet west of a northeast corner of grantors property.

Thence in a southerly direction bearing south 00° 45' west a distance of 130 feet to a Texas Power & Light Company pole. Thence continuing in the same southerly direction a distance of 150 feet to a Texas Power & Light Company angle pole with an angle of 02° 15' and its attached angle guy. Said guy to extend in an easterly direction a distance of 28 feet to a guy anchorage.

Thence continuing in a southerly direction bearing south 03° 00' west a distance of 185 feet to a Texas Power & Light Company angle pole and its attached guys. One guy to extend in an easterly direction a distance of 28 feet to a guy anchorage. One guy to extend in a southerly direction a distance of 28 feet to a guy anchorage.

Thence in a northwesterly direction bearing north 51° 15' west a distance of 175 feet to a Texas Power & Light Company angle pole, an angle of 59° 40' left and its attached guy. Said guy to extend in a northerly direction a distance of 28 feet to a guy anchorage.

Thence in a southwesterly direction bearing south 69° 05' west a distance of 105 feet to a Texas Power & Light Company deadend pole and its attached guys. One guy to extend in the same southwesterly direction a distance of 28 feet to a guy anchorage. One guy to extend in a southerly direction a distance of 28 feet to a guy anchorage.

This description is based on a preliminary survey, and it is understood that Grantees may relocate said lines in the same general direction before or at any time after construction.

Grantees shall have the right to erect 5 poles, 0 stubs, and 6 guy anchorages along the course of said line, together with the right of ingress and egress for the purpose of construction, improving, inspecting, maintaining, operating and removing said lines and appurtenances; the right to relocate said lines in the same relative position to any adjacent road if and when said road is widened in the future, and the right at all times to cut away and keep clear of said lines and appurtenances all trees and other obstructions which, in the sole judgment of Grantees, may endanger or interfere with the proper maintenance and operation of said lines.

TO HAVE AND TO HOLD the above described easement and right unto the said Grantees, their successors and assigns, until all of said lines shall be abandoned.

EXECUTED this 30th day of September, A.D. 19 70.

Robert McKeethan

Authentisign ID: 0892CC4F-2BC8-F111-BF5B-000D3A4FF82A

VOL 1354 PAGE 52 CERTIFICATE OF ACKNOWLEDGMENT FOR INDIVIDUALS

THE STATE OF TEXAS

County of Smith

BEFORE ME, the undersigned authority, on this day personally appeared

Robert McKeethan

known to me to be the person(s) whose name(s) is (are) subscribed to the foregoing instrument, and acknowledged to me that he executed the same for the purposes and consideration therein expressed.

GIVEN UNDER MY HAND AND SEAL OF OFFICE this 30th day of September A. D. 1970

T. O. Jordan

Notary Public Smith County, Texas

4-21-4-3088-340

THE STATE OF TEXAS

County of

I hereby certify that this instrument was filed for record in my office at 9:20 o'clock A.M., and duly recorded by me in Book 1354 of the Deed Records of said County, at page 52

Given under my hand and seal of office this 23rd day of December 1970

County Clerk, Smith County, Texas

By Deputy

Easement and Right of Way

Texas Power & Light Co.

STATE OF TEXAS, County of

I, County Clerk in and for said County, hereby certify that the within Conveyance was filed in my office for record on the day of 19

County Clerk in and for said County, Texas

By Deputy

TEXAS POWER & LIGHT COMPANY
REAL ESTATE & RIGHT-OF-WAY
P. O. BOX 6331
DALLAS, TEXAS 75222

32

FILED
ERNEST CHRISTIAN
COUNTY CLERK
SMITH COUNTY, TEXAS
DEPUTY
DEC 23 9 20 AM '70

FILED AT 9:20 O'CLOCK A M. ON THE 23 DAY OF Dec 1970

RECORDED AT 1:30 O'CLOCK P M. ON THE 23 DAY OF Dec 1970

ERNEST CHRISTIAN, COUNTY CLERK, BY Evelyn Brand DEPUTY

1 of 1

W.A. 3088
E.R. 5
Proj. 131
Code 420/88

Form SR-4-1-69

THE STATE OF TEXAS

County of Smith

12701

KNOW ALL MEN BY THESE PRESENTS:

That George McCrary

of Smith County, Texas, hereinafter called "Grantor", whether one or more, in consideration of the advantages which will accrue to Grantor from the construction of the electric power line hereinafter described, hereby grants to TEXAS POWER & LIGHT COMPANY, of Dallas, Texas, an easement and right of way for an electric power line consisting of a variable number of wires and one or more electric circuits, and all necessary or desirable appurtenances, and for a communication line and appurtenances, upon, over and across Grantor's land in the Woodson Henry Survey, Abstract No. 429, Smith County, Texas.

The center line of said power line shall be located across said land as follows:

Beginning at an existing Texas Power & Light Company line pole in grantors northeast property corner. Said pole being located 50 feet south of grantors north property line and 30 feet west of grantors east property line.

Thence in a southeasterly direction a distance of 45 feet to a pole and its attached guy. Said guy to extend in a northerly direction a distance of 30 feet to its attached anchor.

Thence in a southerly direction a distance of 145 feet to a pole.

Thence in a southerly direction a distance of 165 feet to a pole and its attached guy. Said guy to extend in a southerly direction a distance of 30 feet to its attached anchor.